
SUPPLY SCOPE (distributor quantities issue, no prices): we supply the pre-cut Nudura ICF forms only; the stock forms, accessories and alignment system are supplied by the distributor. All other structure and information shown is supplied in good faith for coordination only and must be checked by the relevant professional.

QUOTATION - NOT FOR CONSTRUCTION

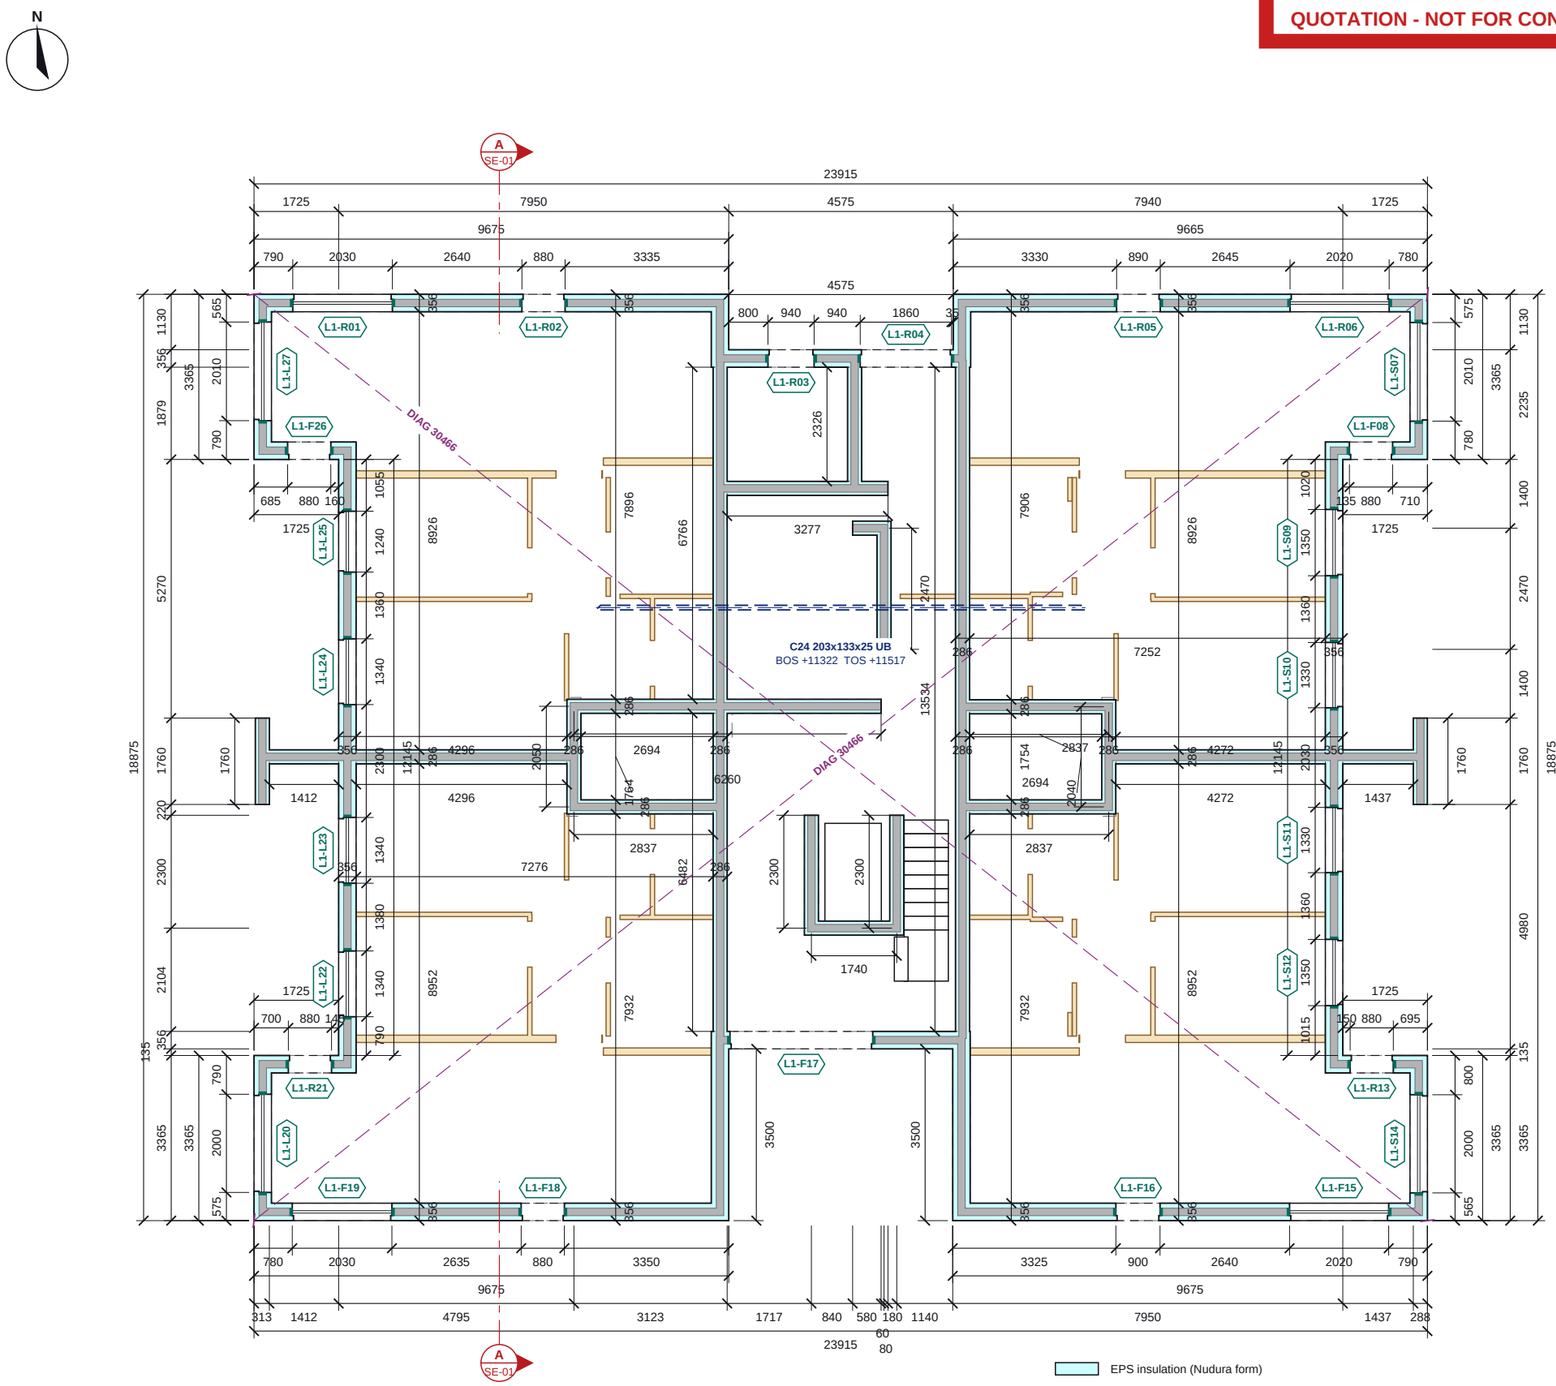

GROUND FLOOR ICF PLAN

Scale 1:125 @ A3 | Plan cut at +1480

GROUND FLOOR ICF SCHEDULES

OPENING SCHEDULE

Ref	Width	Height	Sill	Head	Lintel
L1-R01	2030	1950	+130	+2080	-
L1-R02	880	2080	0	+2080	-
L1-R03	940	2084	0	+2084	-
L1-R04	1860	2080	0	+2080	-
L1-R05	890	2080	0	+2080	-
L1-R06	2020	1950	+130	+2080	-
L1-S07	2010	1950	+130	+2080	-
L1-F08	880	2084	0	+2084	-
L1-S09	1350	1500	+580	+2080	-
L1-S10	1330	1500	+580	+2080	-
L1-S11	1330	1500	+580	+2080	-
L1-S12	1350	1500	+580	+2080	-
L1-R13	880	2084	0	+2084	-
L1-S14	2000	1950	+130	+2080	-
L1-F15	2020	1950	+130	+2080	-
L1-F16	900	2080	0	+2080	-
L1-F17	2910	2414	0	+2414	-
L1-F18	880	2080	0	+2080	-
L1-F19	2030	1950	+130	+2080	-
L1-L20	2000	1950	+130	+2080	-
L1-R21	880	2084	0	+2084	-
L1-L22	1340	1500	+580	+2080	-
L1-L23	1340	1500	+580	+2080	-
L1-L24	1340	1500	+580	+2080	-
L1-L25	1240	1500	+580	+2080	-
L1-F26	880	2084	0	+2084	-
L1-L27	2010	1950	+130	+2080	-

Structural openings in the ICF; sill and head above GF FFL.

STEEL SCHEDULE

Mark	Section (engineer)	BOS	TOS
C24	203x133x25 UB S355	+11322	+11517

BOS / TOS = bottom / top of steel above GF FFL (C-1 columns: base / top).

NOTES

1. ICF: Nudura 6" XR35, 101.6 EPS + 152.4 core + 101.6 EPS = 355.6; 6" Std, 66.7 EPS + 152.4 core + 66.7 EPS = 285.8. Dimensions to the ICF faces.
2. Levels above GF FFL. Sill / head = structural opening in the ICF.
3. No structural design exists yet. ICF per the quotation models: 6in XR35 external walls, 6in Standard compartment (party) and core / lift walls; foundation ICF 2 courses below FFL +6.080 on both blocks; FF / SF floors are the drawn 215 metal-deck composite slabs bearing into the ICF core - for the engineer's review.
4. Lintel (L-n) and steel (B-n, C-1) marks from rev -, which takes precedence.
5. Masonry walls shown for context.
6. Steel over dashed. BOS / TOS = bottom / top of steel above GF FFL.

REVISIONS

REV	DATE	DESCRIPTION
Q01	19.10.26	First issue

Nudura™ BuildEase

CLIENT	PROJECT
Ian Piercy (Distributor) for Ramsey Town Commissioners	Close Woirrey / Albert Road, Ramsey, Isle of Man

DRAWING TITLE

BLOCK 1 (12 FLATS) - GROUND FLOOR ICF

ICF walls, openings, lintels, steel over and engineer's notes

SCALE	SIZE	DATE
1:125	A3	19.10.26
DRAWN	CHECKED	APPROVED
TS		

STATUS	DRAWING No.	REV
QUOTATION	ES26-071-GA-02	Q01

Do not scale. All dimensions in millimetres, levels in metres from GF FFL. Check all dimensions on site.