SUPPLY SCOPE (distributor quantities issue, no prices): we supply the pre-cut Nudura ICF forms only; the stock forms, accessories and alignment system are supplied by the distributor. All other structure and information shown is supplied in good faith for coordination only and must be checked by the relevant professional.

QUOTATION - NOT FOR CONSTRUCTION

SECTION A-A (x = 6,326 in the block frame, 1:100)

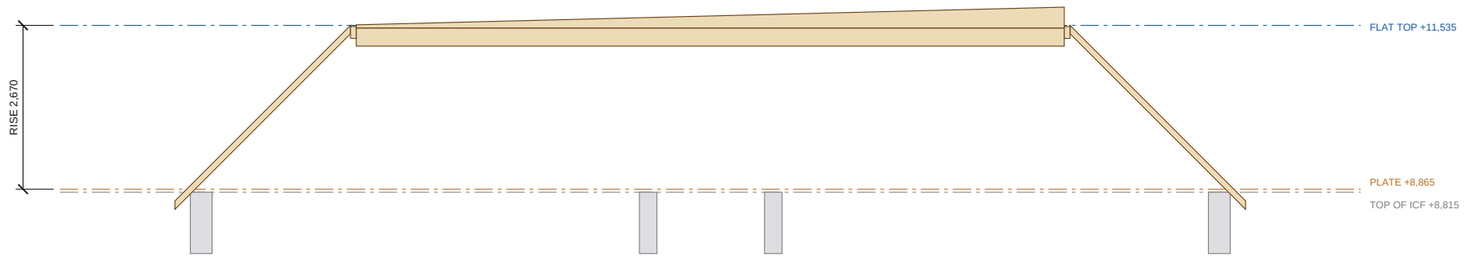

SECTION B-B (y = 10,202 in the block frame, 1:150)

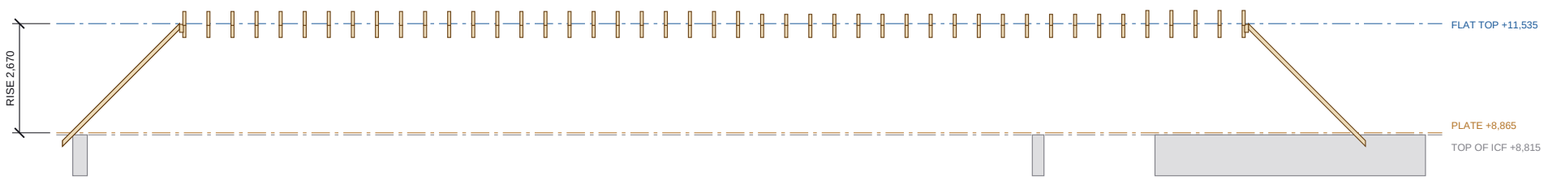

ROOF SECTIONS

Scale AS SHOWN @ A3 | A: across the left wing; B: through the middle of the block (the link); seen from the front / left

ROOF MEMBERS BY ROLE

MEMBERS BY ROLE

Role	Section(s)	Length	Qty
Ceiling joist	75x295 C24	6,239-13,464	45
Common rafter	47.0x97.0 C24	2,733-4,047	123
Cripple rafter	47.0x97.0 C24	834-3,910	51
Firring	75x115-271 firring, 75x27-36	6,239-13,464	45
Hip	47x147 C24	1,414-4,956	20
Jack rafter (hip)	47.0x97.0 C24	768-3,497	94
Jack rafter (valley)	47.0x97.0 C24	768-2,291	18
Ridge beam	2/47x195 C24	2,540-13,842	12
Ridge board	47x122 C24	1,725	6
Valley	63x147 C24	3,347-4,956	10
osb	18 OSB3 deck	0	1
Total members			**425**

NOTES

1. FOR SUPPLIER QUOTES ONLY. Sections drawn from the quotation model member geometry (BuildEase roof framer, cut roof). The drawing (06-001A) shows a trussed roof with a flat top: the truss manufacturer designs the final trusses / girders / jack sets (members, joints, plates, bracing) to BS EN 1995-1-1 and confirms all sizes.
2. 45 deg pitch, wall plate +8,865, flat top +11,535 (PV panels and the counter-balanced handrail by others), overhang 250.
3. Design brief (to be confirmed): natural / imitation slate on battens and breathable membrane, plasterboard ceiling, loft not habitable, PV array on the flat top; Ramsey IoM, coastal, ~6 m AOD: snow zone 1, vb 26 m/s, exposed.
4. Plan, metalwork and the loose-timber totals on ES26-071-RF-03.

REVISIONS

REV	DATE	DESCRIPTION
Q01	19.10.26	First issue

Nudura™ BuildEase

CLIENT	PROJECT
Ian Piercy (Distributor) for Ramsey Town Commissioners	Close Woirrey / Albert Road, Ramsey, Isle of Man

DRAWING TITLE

BLOCK 2 (18 FLATS) - ROOF SECTIONS AND MEMBER SCHEDULE

SCALE	SIZE	DATE
AS SHOWN	A3	19.10.26
DRAWN	CHECKED	APPROVED
TS		

STATUS	DRAWING No.	REV
QUOTATION	ES26-071-RF-04	Q01

Do not scale. All dimensions in mm. Check all dimensions on site.