
SUPPLY SCOPE (distributor quantities issue, no prices): we supply the pre-cut Nudura ICF forms only; the stock forms, accessories and alignment system are supplied by the distributor. All other structure and information shown is supplied in good faith for coordination only and must be checked by the relevant professional.

QUOTATION - NOT FOR CONSTRUCTION

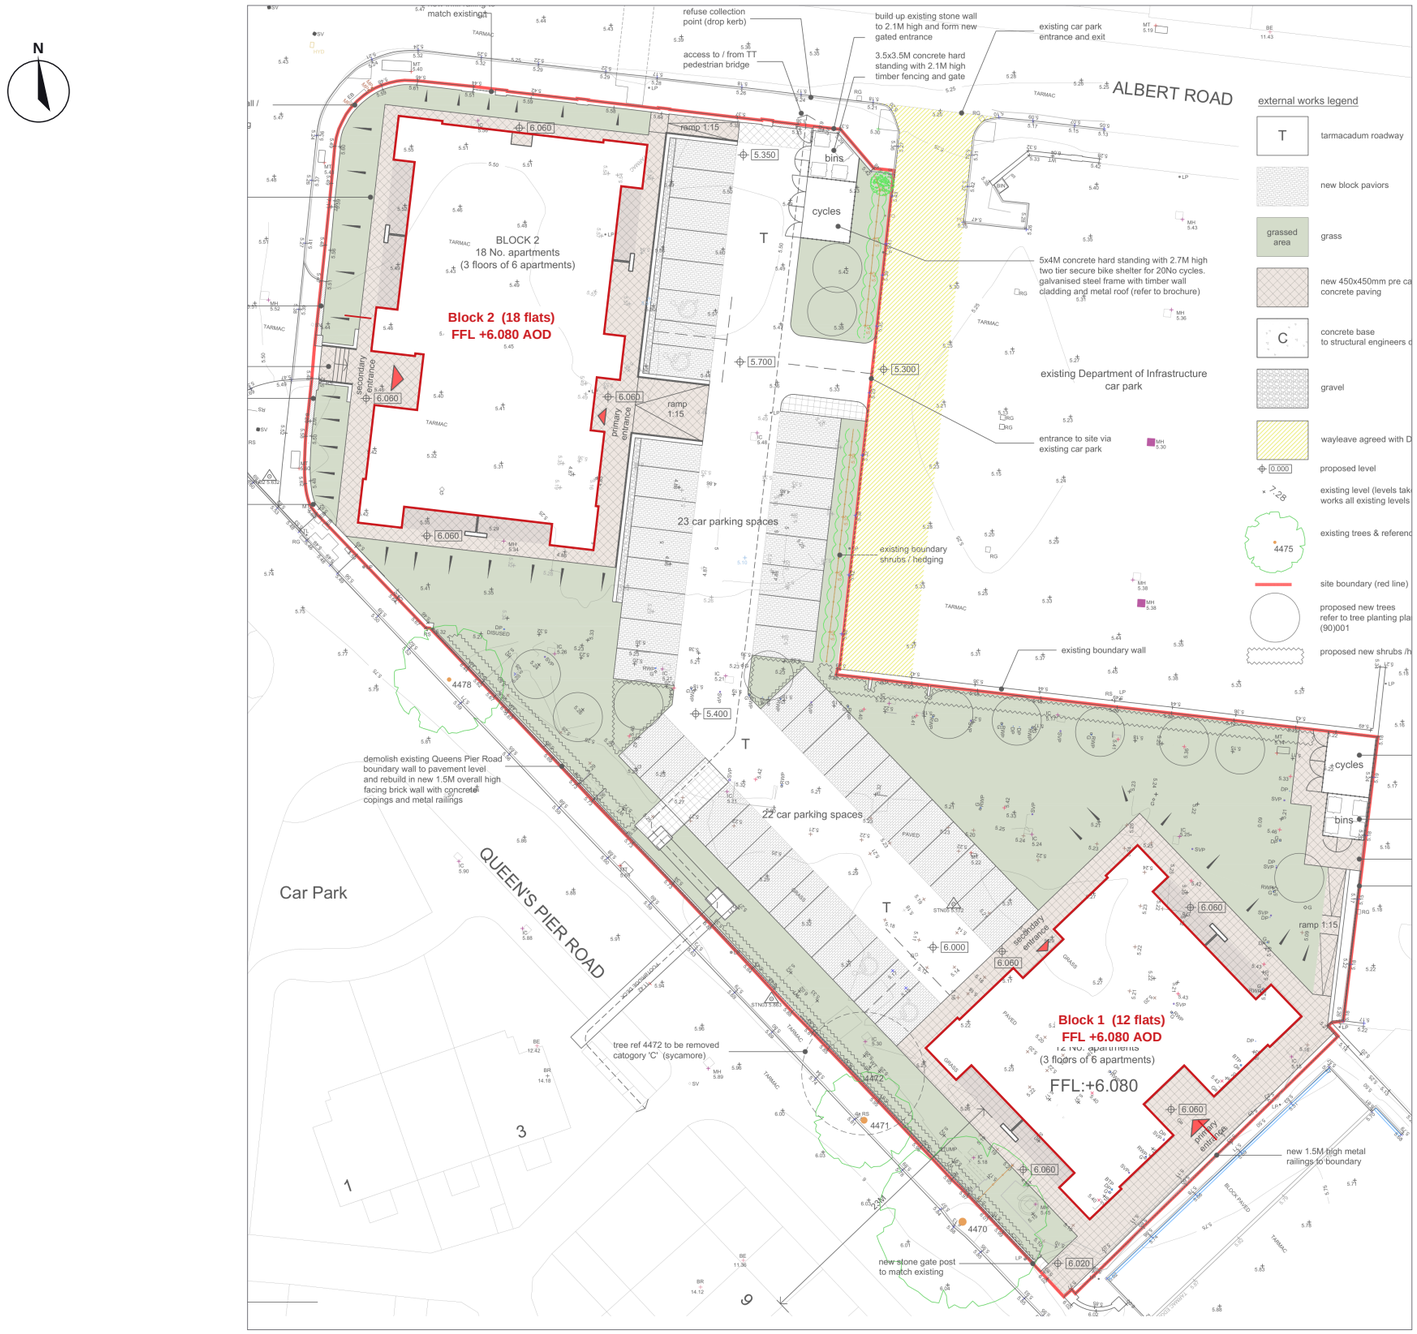

SITE PLAN

Scale 1:500 @ A3 | 00-001A base (architect, PLANNING rev A), ICF blocks in red; tick = front face

0 1 2 3 4 5 6 7 8 9 10 11 12 13 14 15 16 17 18 19 20m

BLOCK SCHEDULE

BLOCKS AND LEVELS

Block	Flats	FFL AOD	Rot deg	Front	Plan m2
Block 1	12	+6.080	43.76	SE	392
Block 2	18	+6.080	-96.66	W	574

FFL AOD = GF finished floor level (m). Rot = the block plan's rotation on the site (anticlockwise from east). Plan m2 = area inside the ground-floor external wall face as modelled.

STOREY LEVELS (BOTH BLOCKS)

Level	Above GF FFL	AOD
GF FFL	0	+6.080
FF FFL	3,090	+9.170
SF FFL	6,165	+12.245
Top of wall plate	8,865	+14.945
Roof flat top	11,535	+17.615
U/S foundation ICF	-914	+5.166

NOTES

1. Base: McGarrigle Ayre drawing 1464 00-001A Proposed Site Plan (PLANNING rev A), reproduced for location only. Block footprints in red are the Nudura ICF quotation models (ground-floor external wall faces) placed on the site plan's block outlines (fit within 150 mm on 99-100 % of the ring).
2. Finished floor levels: both blocks GF FFL +6.080 (00-001A; tidal flood level +5.700). Upper floors FF +9.170 (3,090), SF +12.245 (6,165); top of wall plate +14.945 (8,865), roof flat top +17.615 (11,535) (06-001A). Foundation ICF 2 courses (914.4) below FFL all round, on a strip foundation by others (engineer to design).
3. Block 1: 12 flats, front to Mayfield (SE). Block 2: 18 flats, front to Albert Square (W). Tick = front face.
4. Do not scale for setting out: setting out by others from the architect's dimensioned layout.

REVISIONS

REV	DATE	DESCRIPTION
Q01	19.10.26	First issue

Nudura™ BuildEase

CLIENT	PROJECT
Ian Piercy (Distributor) for Ramsey Town Commissioners	Close Woirrey / Albert Road, Ramsey, Isle of Man

DRAWING TITLE

SITE PLAN - BLOCKS AND FLOOR LEVELS

00-001A site plan with the two ICF blocks and floor levels

SCALE	SIZE	DATE
AS SHOWN	A3	19.10.26
DRAWN: TS	CHECKED	APPROVED

STATUS	DRAWING No.	REV
QUOTATION	ES26-071-SP-01	Q01

Do not scale. All dimensions in mm. Check all dimensions on site.